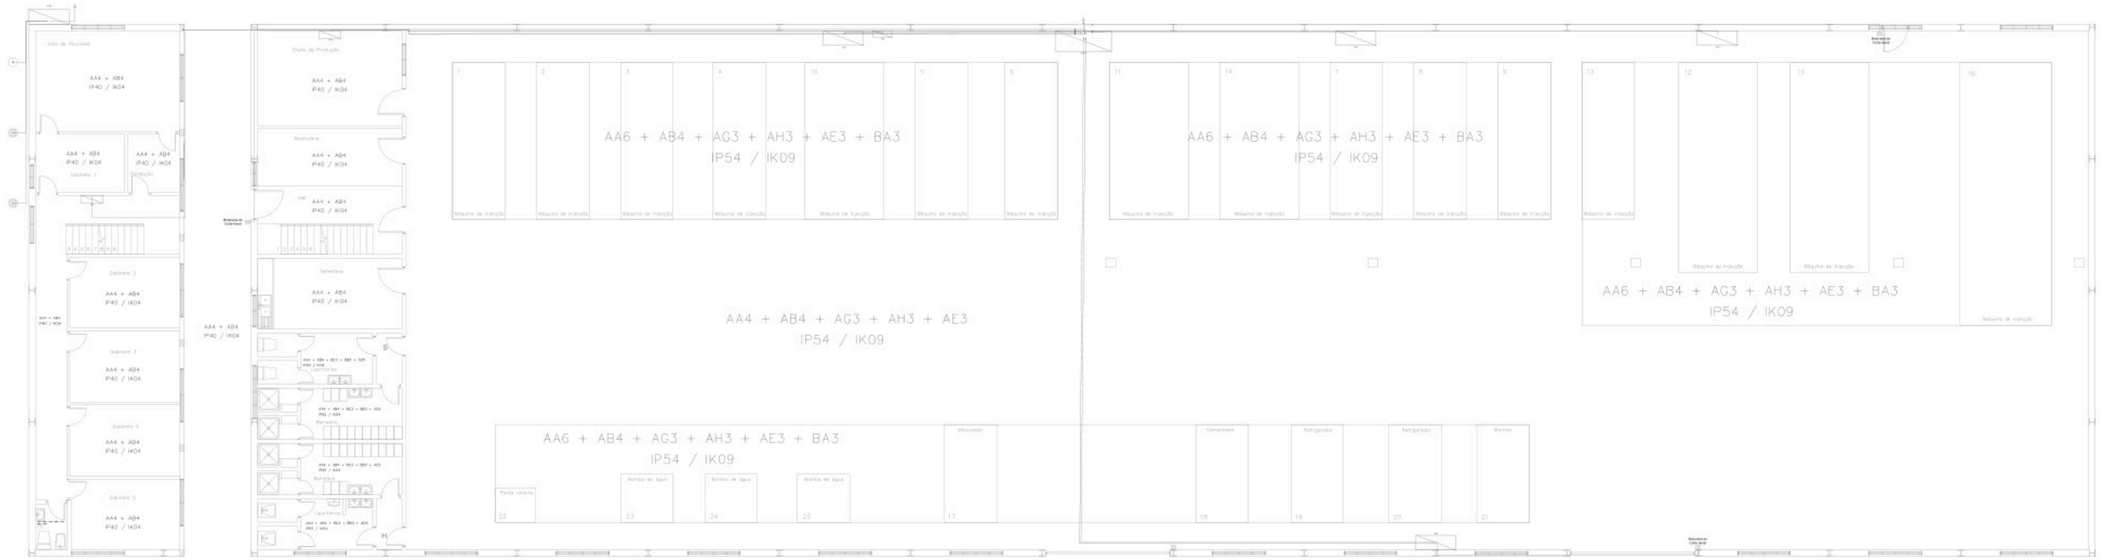


PLAN 08 — Alimentation des tableaux et bornes IRVE rez de chaussee

Reproduction graphique anonymisée d’un document de référence (2023).

Équipe d’analyse : Moustapha IBRAHIM DJAMA · Thomas DHUNARA · Mariel FRESNEL

Plan original non attribuable à cette équipe. Les libellés techniques non traduits proviennent du plan source. Vérifier tous les choix avant utilisation.