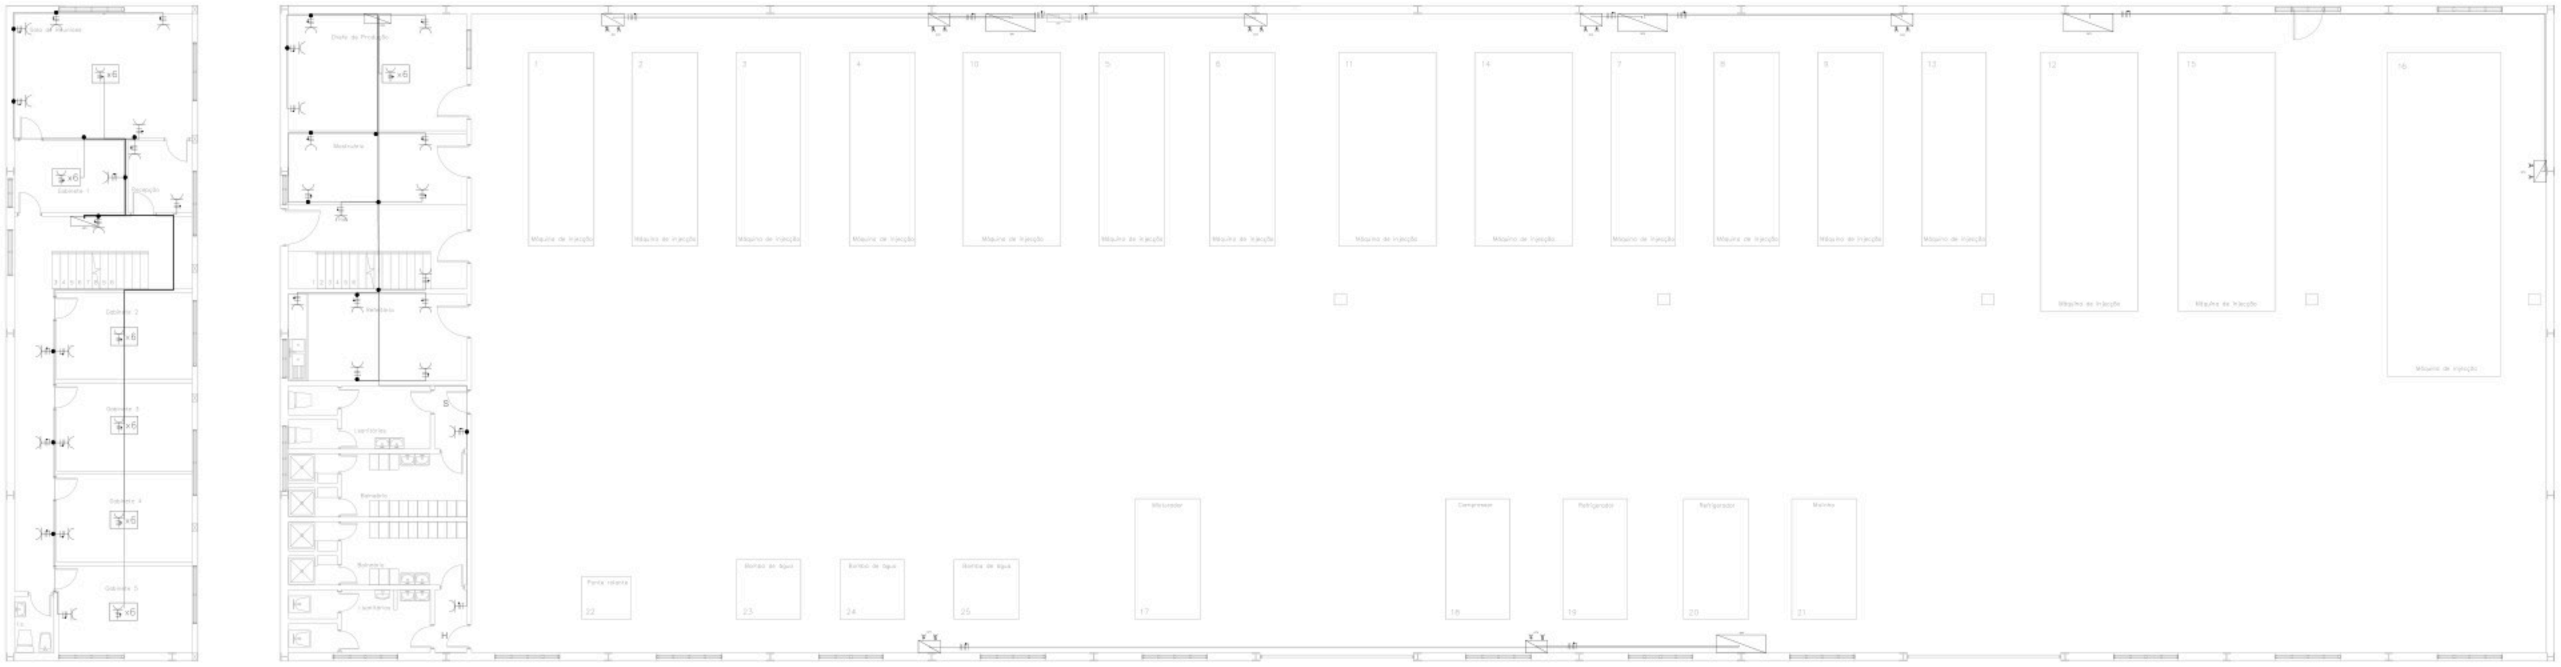

Simbolo	Legenda
	Quadro Elétrico
	Representação do condutor de 1 condutor de fase, 1 condutor e neutro e 1 condutor de terra de proteção
	Quadro de Tomadas
	Caixa de Tomadas(Embutida no Pavimento Técnico)
	Tomada Monofásica do Tipo Schuko
	Representação do condutor de 3 condutor de fase, 1 condutor e neutro e 1 condutor de terra de proteção

PLAN 21 — Circuits de prises rez de chaussee

Reproduction graphique anonymisée d’un document de référence (2023).

Équipe d’analyse : Moustapha IBRAHIM DJAMA · Thomas DHUNARA · Mariel FRESNEL

Plan original non attribuable à cette équipe. Les libellés techniques non traduits proviennent du plan source. Vérifier tous les choix avant utilisation.